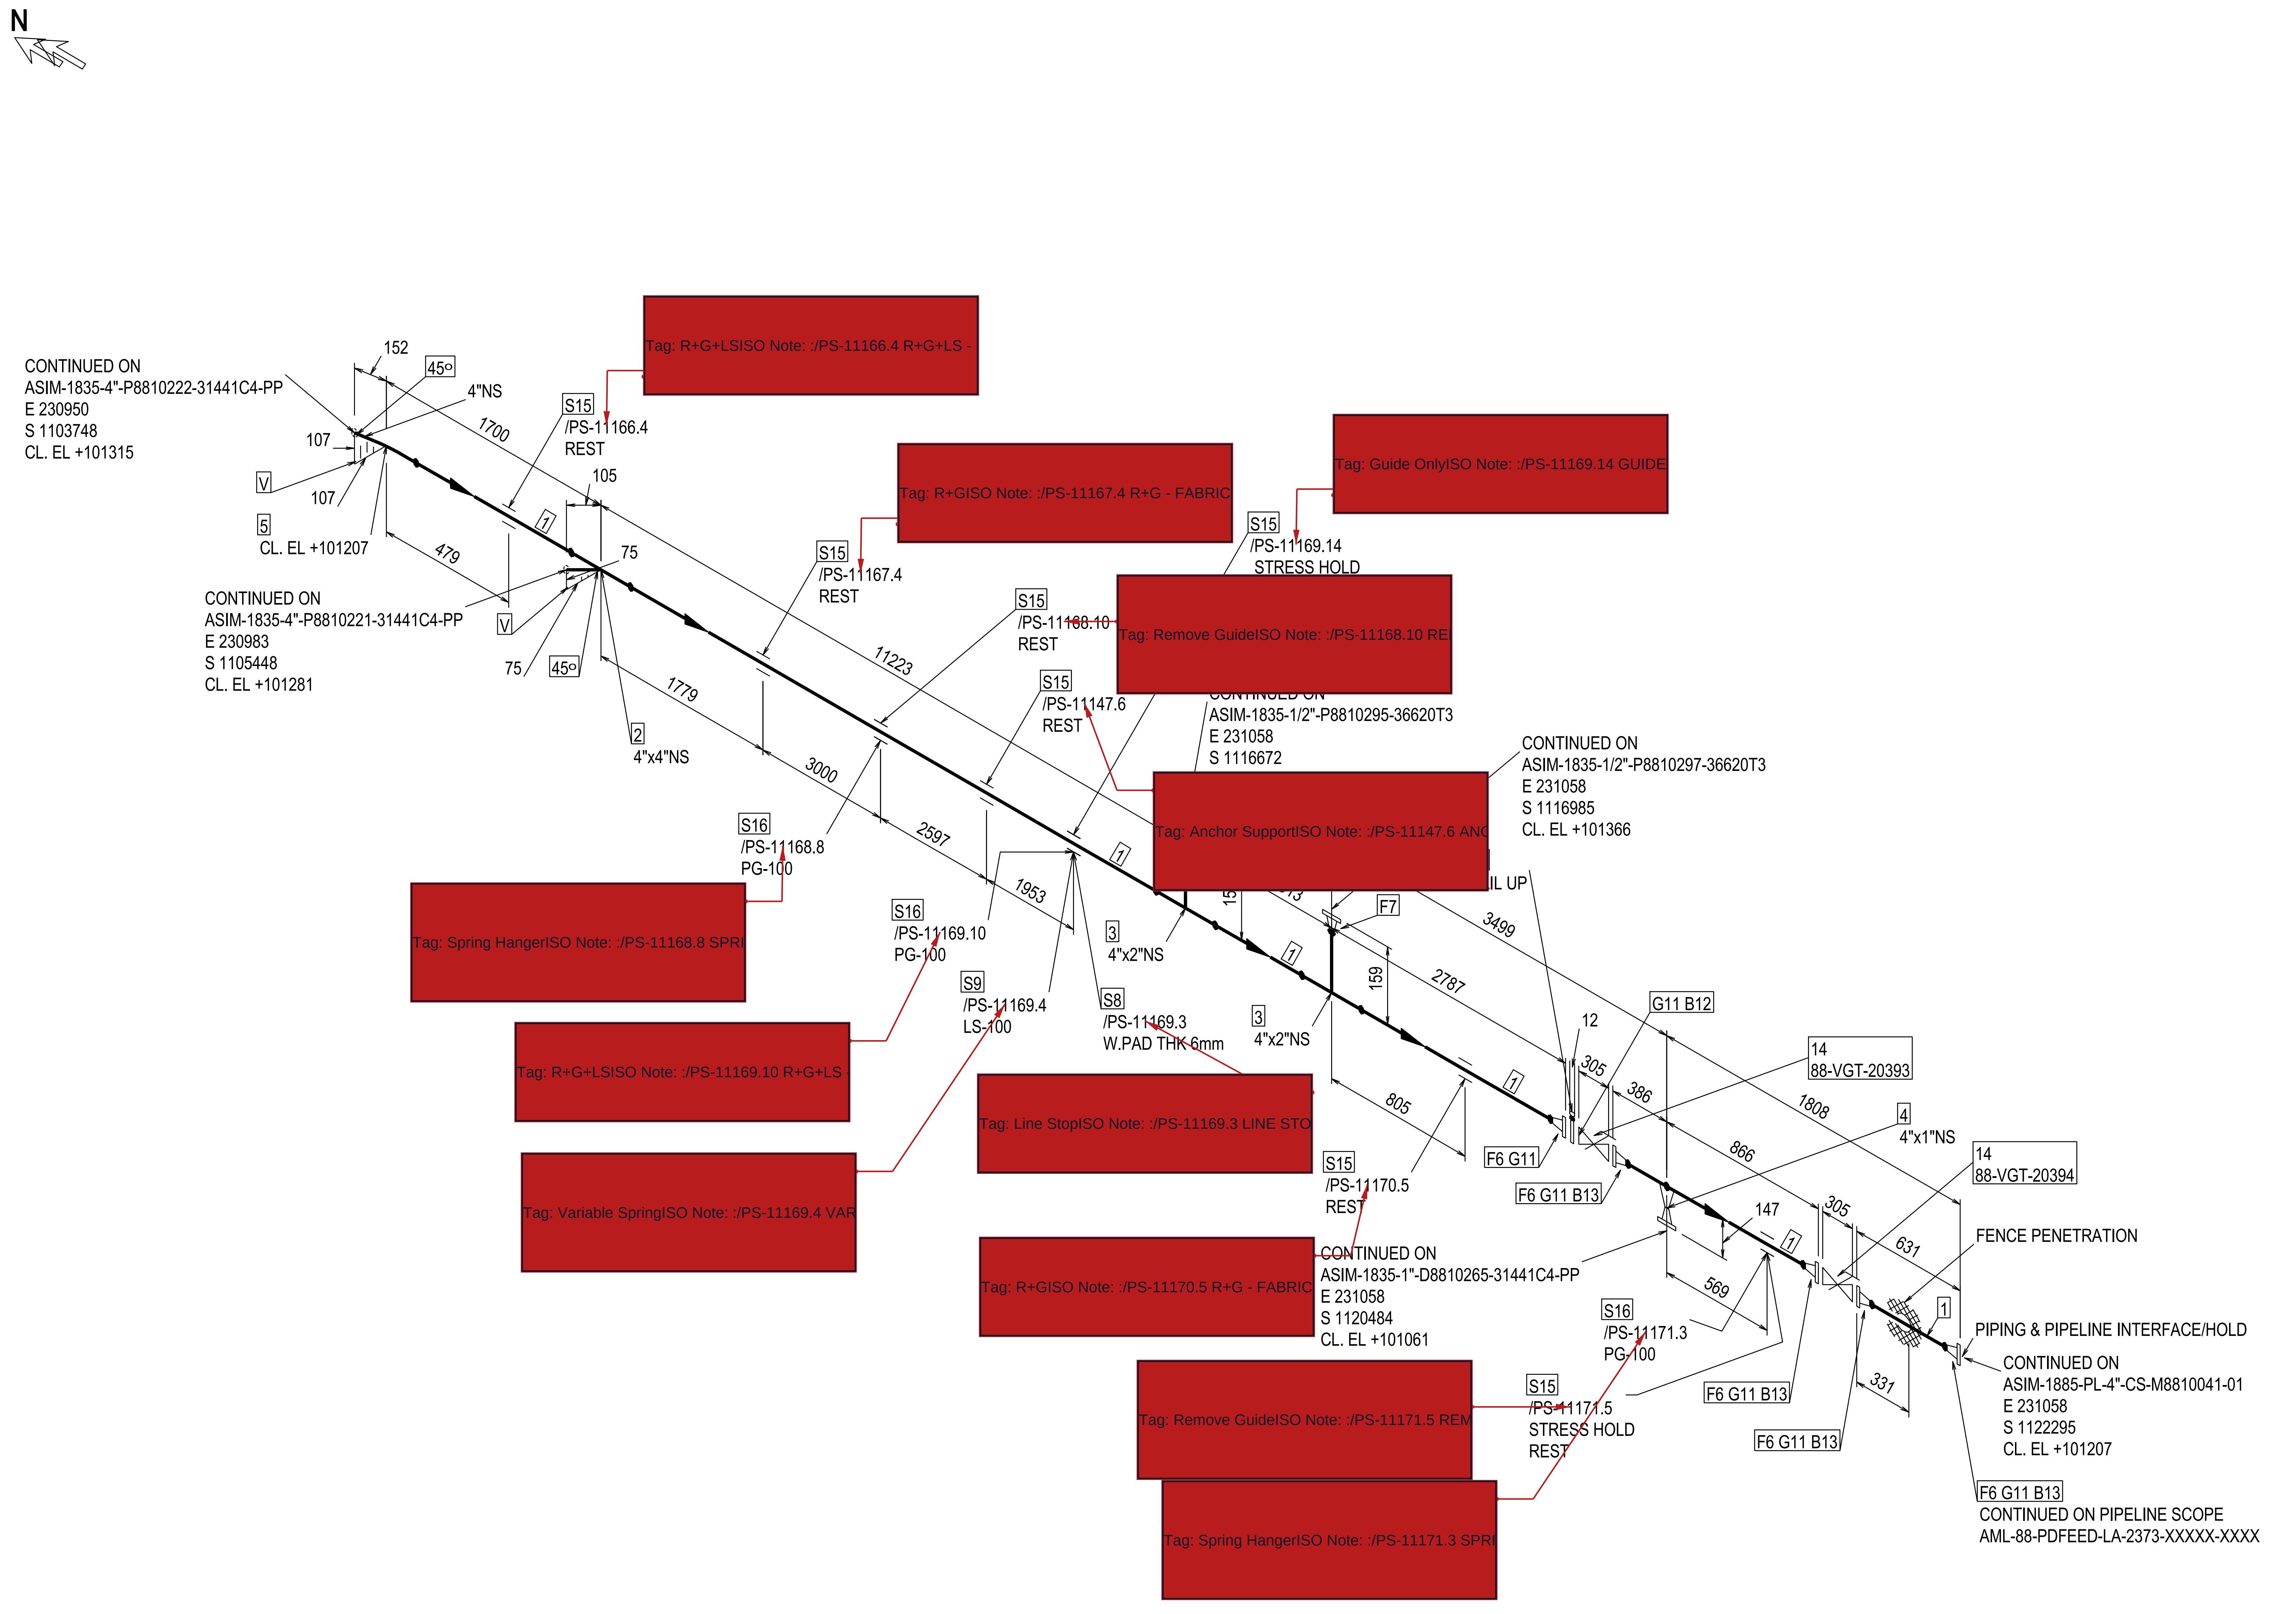
N
CONTINUED ON
ASIM-1835-4"-P8810222-31441C4-PP
E 230950
S 1103748
CL. EL +101315
152
45°
4"NS
107
107
V
5
CL. EL +101207
1700
S15
/PS-11166.4
REST
105
1
75
479
CONTINUED ON
ASIM-1835-4"-P8810221-31441C4-PP
E 230983
S 1105448
CL. EL +101281
V
75
45°
1779
2
4"x4"NS
3000
Tag: R+G+LSISO Note: :/PS-11166.4 R+G+LS -
Tag: R+GISO Note: :/PS-11167.4 R+G - FABRIC
S15
/PS-11167.4
REST
11223
S15
/PS-11168.10
REST
Tag: Remove GuideISO Note: :/PS-11168.10 REI
S15
/PS-11147.6
REST
Tag: Guide OnlyISO Note: :/PS-11169.14 GUIDE
S15
/PS-11169.14
STRESS HOLD
CONTINUED ON
ASIM-1835-1/2"-P8810295-36620T3
E 231058
S 1116672
Tag: Anchor SupportISO Note: :/PS-11147.6 ANC
CONTINUED ON
ASIM-1835-1/2"-P8810297-36620T3
E 231058
S 1116985
CL. EL +101366
S16
/PS-11168.8
PG-100
Tag: Spring HangerISO Note: :/PS-11168.8 SPRI
2597
1953
1
S16
/PS-11169.10
PG-100
3
4"x2"NS
IL UP
F7
3499
159
2787
S9
/PS-11169.4
LS-100
S8
/PS-11169.3
W.PAD THK 6mm
3
4"x2"NS
1
Tag: R+G+LSISO Note: :/PS-11169.10 R+G+LS -
Tag: Line StopISO Note: :/PS-11169.3 LINE STO
Tag: Variable SpringISO Note: :/PS-11169.4 VAR
805
12
G11 B12
305
386
14
88-VGT-20393
1808
F6 G11
F6 G11 B13
866
4
4"x1"NS
14
88-VGT-20394
S15
/PS-11170.5
REST
147
305
1
631
FENCE PENETRATION
Tag: R+GISO Note: :/PS-11170.5 R+G - FABRIC
CONTINUED ON
ASIM-1835-1"-D8810265-31441C4-PP
E 231058
S 1120484
CL. EL +101061
569
S16
/PS-11171.3
PG-100
1
PIPING & PIPELINE INTERFACE/HOLD
CONTINUED ON
ASIM-1885-PL-4"-CS-M8810041-01
E 231058
S 1122295
CL. EL +101207
Tag: Remove GuideISO Note: :/PS-11171.5 REM
S15
/PS-11171.5
STRESS HOLD
REST
F6 G11 B13
331
F6 G11 B13
Tag: Spring HangerISO Note: :/PS-11171.3 SPRI
F6 G11 B13
CONTINUED ON PIPELINE SCOPE
AML-88-PDFEED-LA-2373-XXXXX-XXXX

FABRICATION MATERIALS

PT NO	COMPONENT DESCRIPTION	SIZE (Inch)	ITEM CODE	QTY
	PIPE			
1	PIPE Sch 120 ASTM A106-B	4	74.30.03.159.1	16.7m
	FITTINGS			
2	TEE EQUAL BW Sch 120 ASTM A234-WPB	4 x 4	76.30.81.650.1	1
3	TEE REDUCING BW Sch 120 X Sch 160 ASTM A234-WPB	4 x 2	76.30.88.161.1	2
4	BRANCH FITTING PLAIN Sch 120xXXS ASTM A105	4 x 1	76.72.69.361.1	1
5	ELBOW 90 DEG LR BW Sch 120 ASTM A234-WPB	4	76.30.42.650.1	1
	FLANGES			
6	WELDING NECK FLANGE Sch 120 300# ASTM A105	4	76.62.78.634.1	5
7	WELDING NECK FLANGE Sch 160 300# ASTM A105	2	76.62.78.660.1	2
	PIPE ANNOTATIONS			
8	WEAR PLATE TYPE-421 PAD L 550mm	4		1
9	PIPE STOP TYPE-602	4		1

ERECTION MATERIALS

PT NO	COMPONENT DESCRIPTION	SIZE (Inch)	ITEM CODE	QTY
	FITTINGS			
10	Spectacle blind 300# ASTM A516-60/65/70	4	76.89.62.054.1	1
	GASKETS			
11	GASKET SPIRAL WOUND 300# AISI 316, Graphite CS centring/SS inner ring	4	85.41.36.370.1	6
	BOLTS			
12	130 STUDBOLT WITH NUTS ASTM A193-B7M/A194-2HM	3/4	81.38.66.334.1	8
13	120 STUDBOLT WITH NUTS ASTM A193-B7M/A194-2HM	3/4	81.38.66.332.1	32
	VALVES / IN-LINE ITEMS			
14	GATE VALVE FLGD 300# Body: ASTM A105/A216-WCB/WCC Trim: Alloy 825	4	77.XK.BP.B07.9	2
	PIPE ANNOTATIONS			
15	Pipe Rest XRT01	4		7
16	GUIDE PDO-TYPE-604A/B - 2 x L50x50x6x80HIGH	4		3

HOLDS :

1. NOT ASSIGNEDELEVATION. LOCATION & SUPPORT HOLD AT PIPELINE/PIPING INTERFACE.
2. INSULATION GASKET
3. WEAR PLATE LENGTH & PIPE STOP LENGTH
4. 88-YIQ-10013/15 VENDOR DRAWING
5. STRESS ANALYSIS

UED ENGINEERING DIRECTORATE

شركة تنمية نفط عمان
Petroleum Development Oman

NOTES:

1. ALL DIMENSIONS, ELEVATIONS & CO-ORDINATES ARE IN MM

MATERIAL	Carbon steel sour					PIPING CLASS	31441C4
INSULATION TYPE	PP	STRESS ANALYSIS	Yes	PAINTING SYSTEM	PCS-2		
INSULATION THICKNESS	50	INSPECTION CLASS	Class-1b	COLOUR	SP-1166		
HEAT TRACING	-	FLUID CATEGORY					
STRESS RELIEVE	-	RATING	300#				

LINE CONDITIONS

	DESIGN	TEST
PRESS kPa (g)	4140	7665
TEMP (°C)	260/5	
TEST TYPE	Water	

REFERENCE DRAWINGS & DOCUMENTS

PEFS	AML-88-PDFEED-PX-2365-00028-0001
STRESS CALC NO	-
GA	AML-88-PDFEED-MP-4033-00010-0017/0016

REVISION DETAILS

REV	DATE	DESCRIPTION	DRN.	CHKD.	APPD.	STRESS APP.	CLIENT APP.
02	25.05.22	APPROVED FOR CONSTRUCTION (WITH HOLDS)	RDR	BS	BS		
01	13.03.22	APPROVED FOR CONSTRUCTION (WITH HOLDS)	RRR	VKR	BS		

PROJECT TITLE
AMAL WEST DEVELOPMENT OFF-PLOT FACILITIES

AREA	PLANT	WBS No.
AMAL WEST	AMAL WEST PHASE 2A3_88-MS-10001A	-

MODEL AREA	LINE No.	PROJECT CODE
ASIM-1835-CU	4"-P8810203-31441C4-PP	SST000AL0329-AC

BY	DATE	BY	DATE	BY	DATE	BY	DATE	BY	DATE
RRR	13.03.22	VKR	13.03.22	BS	13.03.22	TNJ	13.03.22		

DRAWING NO
AML-88-PDFEED-MP-2343-00010-0315

SHEET 1 OF 1
REV 02

www.pdo.co.om

www.pdo.co.om

DATE: 17-6-2026-15:26 PROJ: AML 3.1.7.0 ZONE: ASIM-1835-CU-PI-P USER: MUCL729 PIPE: ASIM-1835-4"-P8810203-31441C4-PP