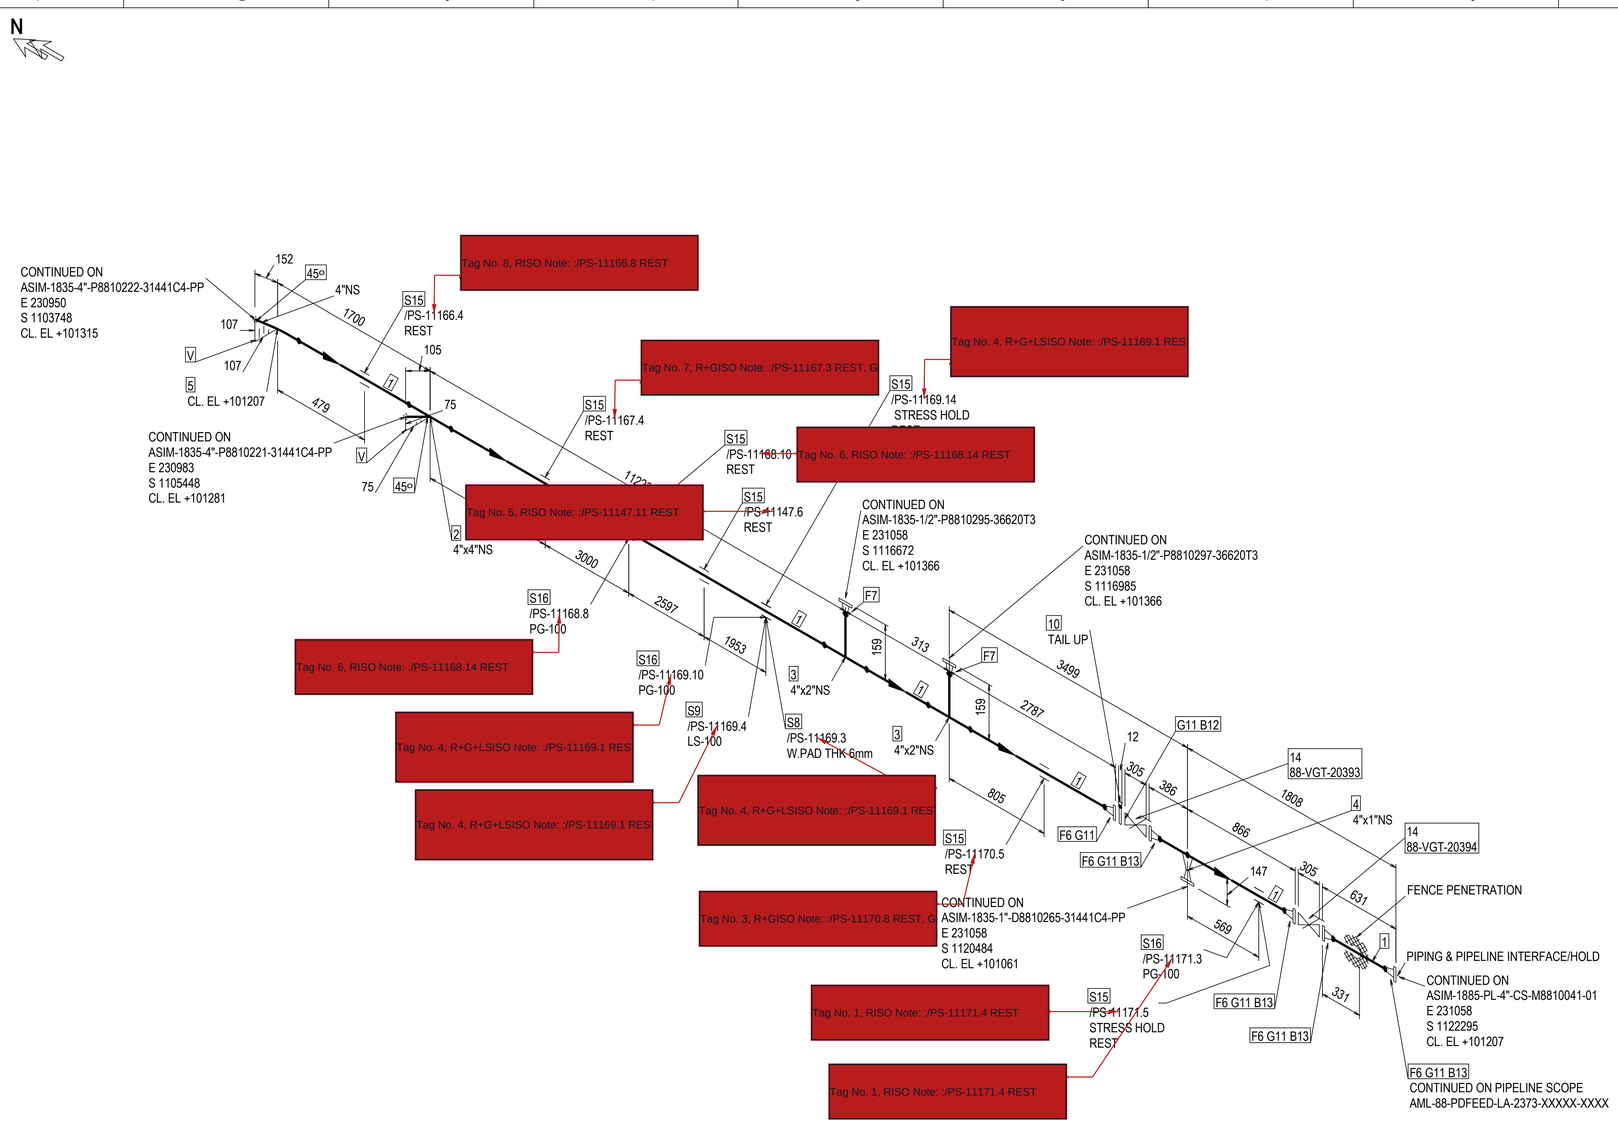


FABRICATION MATERIALS

PT NO	COMPONENT DESCRIPTION	SIZE (Inch)	ITEM CODE	QTY
	PIPE			
1	PIPE Sch 120 ASTM A106-B	4	74.30.03.159.1	16.7m
	FITTINGS			
2	TEE EQUAL BW Sch 120 ASTM A234-WPB	4 x 4	76.30.81.650.1	1
3	TEE REDUCING BW Sch 120 X Sch 160 ASTM A234-WPB	4 x 2	76.30.88.161.1	2
4	BRANCH FITTING PLAIN Sch 120xXXS ASTM A105	4 x 1	76.72.69.361.1	1
5	ELBOW 90 DEG LR BW Sch 120 ASTM A234-WPB	4	76.30.42.650.1	1
	FLANGES			
6	WELDING NECK FLANGE Sch 120 300# ASTM A105	4	76.62.78.634.1	5
7	WELDING NECK FLANGE Sch 160 300# ASTM A105	2	76.62.78.660.1	2
	PIPE ANNOTATIONS			
8	WEAR PLATE TYPE-421 PAD L 550mm	4		1
9	PIPE STOP TYPE-602	4		1

ERECTION MATERIALS

PT NO	COMPONENT DESCRIPTION	SIZE (Inch)	ITEM CODE	QTY
	FITTINGS			
10	Spectacle blind 300# ASTM A516-60/65/70	4	76.89.62.054.1	1
	GASKETS			
11	GASKET SPIRAL WOUND 300# AISI 316, Graphite CS centring/SS inner ring	4	85.41.36.370.1	6
	BOLTS			
12	130 STUDBOLT WITH NUTS ASTM A193-B7M/A194-2HM	3/4	81.38.66.334.1	8
13	120 STUDBOLT WITH NUTS ASTM A193-B7M/A194-2HM	3/4	81.38.66.332.1	32
	VALVES / IN-LINE ITEMS			
14	GATE VALVE FLGD 300# Body: ASTM A105/A216-WCB/WCC Trim: Alloy 825	4	77.XK.BP.B07.9	2
	PIPE ANNOTATIONS			
15	Pipe Rest XRT01	4		7
16	GUIDE PDO-TYPE-604A/B - 2 x L50x50x6x80HIGH	4		3

HOLDS :

1. NOT ASSIGNEDELEVATION. LOCATION & SUPPORT HOLD AT PIPELINE/PIPING INTERFACE.
2. INSULATION GASKET
3. WEAR PLATE LENGTH & PIPE STOP LENGTH
4. 88-YIQ-10013/15 VENDOR DRAWING
5. STRESS ANALYSIS

UED ENGINEERING DIRECTORATE

شركة تنمية نفط عمان
Petroleum Development Oman

NOTES:

1. ALL DIMENSIONS, ELEVATIONS & CO-ORDINATES ARE IN MM

MATERIAL	Carbon steel sour			PIPING CLASS	31441C4
INSULATION TYPE	PP	STRESS ANALYSIS	Yes	PAINTING SYSTEM	PCS-2
INSULATION THICKNESS	50	INSPECTION CLASS	Class-1b	COLOUR	SP-1166
HEAT TRACING	-	FLUID CATEGORY			
STRESS RELIEVE	-	RATING	300#		

LINE CONDITIONS	DESIGN	TEST
PRESS kPa (g)	4140	7665
TEMP (C)	260/5	
TEST TYPE	Water	

										BY	DATE	BY	DATE
PEFS	AML-88-PDFEED-PX-2365-00028-0001	02	25.05.22	APPROVED FOR CONSTRUCTION (WITH HOLDS)	RDR	BS	BS			RRR	13.03.22	VKR	13.03.22
STRESS CALC NO	-	01	13.03.22	APPROVED FOR CONSTRUCTION (WITH HOLDS)	RRR	VKR	BS						
GA	AML-88-PDFEED-MP-4033-00010-0017/0016	REV	DATE	DESCRIPTION	DRN.	CHKD.	APPD.	STRESS APP.	CLIENT APP.				
REFERENCE DRAWINGS & DOCUMENTS		REVISION DETAILS											

BY	DATE	BY	DATE	BY	DATE	BY	DATE	BY	DATE	BY	DATE	BY	DATE
BS	13.03.22	TNJ	13.03.22										

PROJECT TITLE
AMAL WEST DEVELOPMENT OFF-PLOT FACILITIES

AREA	PLANT	WBS No.
AMAL WEST	AMAL WEST PHASE 2A3_88-MS-10001A	-
MODEL AREA	LINE No.	PROJECT CODE
ASIM-1835-CU	4"-P8810203-31441C4-PP	SST000AL0329-AC

DRAWING NO
AML-88-PDFEED-MP-2343-00010-0315

SHEET 1 OF 1 | REV 02

www.pdo.co.om

DATE: 17-6-2026-15:26 PROJ: AML 3.1.7.0 ZONE: ASIM-1835-CU-PI-P USER: MUCL729 PIPE: ASIM-1835-4"-P8810203-31441C4-PP