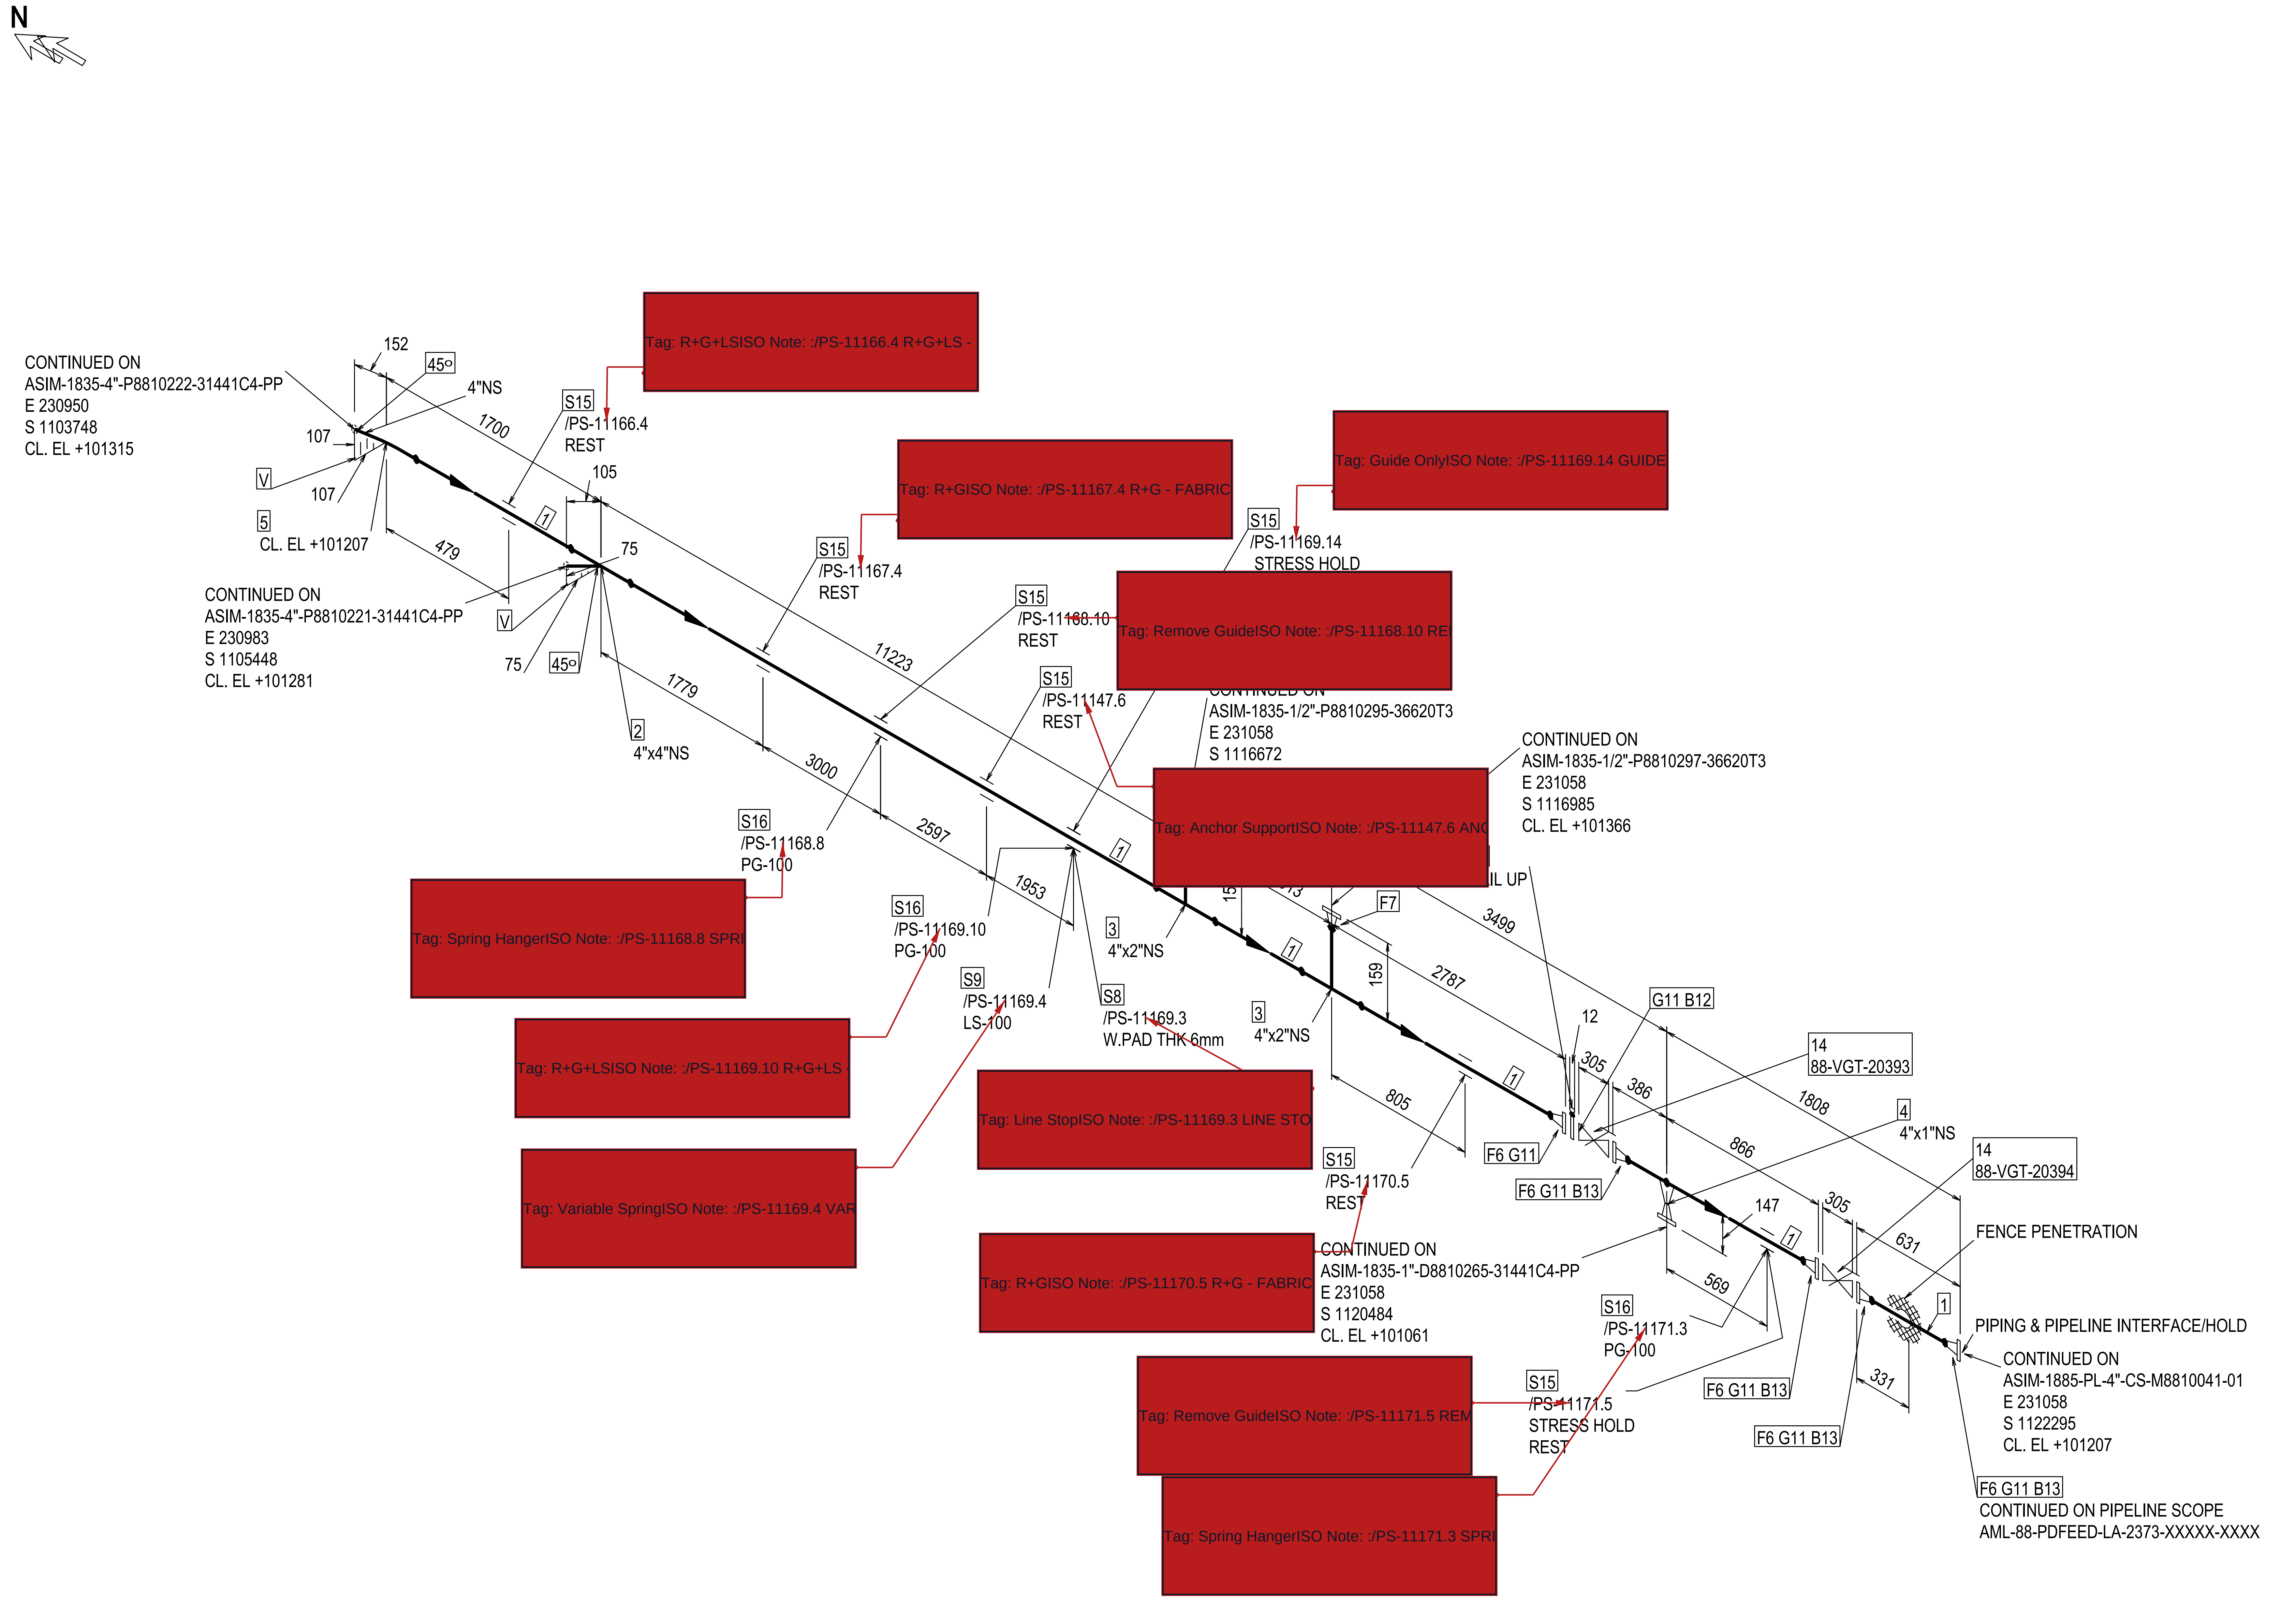
N
CONTINUED ON
ASIM-1835-4"-P8810222-31441C4-PP
E 230950
S 1103748
CL. EL +101315
152
45o
4"NS
1700
107
V
107
5
CL. EL +101207
479
S15
/PS-11166.4
REST
Tag: R+G+LSISO Note: :/PS-11166.4 R+G+LS -
105
1
75
CONTINUED ON
ASIM-1835-4"-P8810221-31441C4-PP
E 230983
S 1105448
CL. EL +101281
V
75
45o
1779
2
4"x4"NS
S15
/PS-11167.4
REST
Tag: R+GISO Note: :/PS-11167.4 R+G - FABRIC
11223
S15
/PS-11169.14
STRESS HOLD
Tag: Guide OnlyISO Note: :/PS-11169.14 GUIDE
S15
/PS-11168.10
REST
Tag: Remove GuideISO Note: :/PS-11168.10 RE
S15
/PS-11147.6
REST
ASIM-1835-1/2"-P8810295-36620T3
E 231058
S 1116672
CONTINUED ON
ASIM-1835-1/2"-P8810297-36620T3
E 231058
S 1116985
CL. EL +101366
Tag: Anchor SupportISO Note: :/PS-11147.6 ANC
3000
2597
1953
S16
/PS-11168.8
PG-100
Tag: Spring HangerISO Note: :/PS-11168.8 SPRI
S16
/PS-11169.10
PG-100
Tag: R+G+LSISO Note: :/PS-11169.10 R+G+LS
S9
/PS-11169.4
LS-100
Tag: Variable SpringISO Note: :/PS-11169.4 VAR
3
4"x2"NS
S8
/PS-11169.3
W.PAD THK 6mm
Tag: Line StopISO Note: :/PS-11169.3 LINE STO
IL UP
F7
3499
159
2787
3
4"x2"NS
805
12
G11 B12
305
386
14
88-VGT-20393
1808
F6 G11
F6 G11 B13
866
4
4"x1"NS
14
88-VGT-20394
S15
/PS-11170.5
REST
Tag: R+GISO Note: :/PS-11170.5 R+G - FABRIC
147
305
631
FENCE PENETRATION
CONTINUED ON
ASIM-1835-1"-D8810265-31441C4-PP
E 231058
S 1120484
CL. EL +101061
569
S16
/PS-11171.3
PG-100
1
PIPING & PIPELINE INTERFACE/HOLD
CONTINUED ON
ASIM-1885-PL-4"-CS-M8810041-01
E 231058
S 1122295
CL. EL +101207
S15
/PS-11171.5
STRESS HOLD
REST
Tag: Remove GuideISO Note: :/PS-11171.5 REM
F6 G11 B13
331
F6 G11 B13
Tag: Spring HangerISO Note: :/PS-11171.3 SPRI
F6 G11 B13
CONTINUED ON PIPELINE SCOPE
AML-88-PDFEED-LA-2373-XXXXX-XXXX

FABRICATION MATERIALS

PT NO	COMPONENT DESCRIPTION	SIZE (Inch)	ITEM CODE	QTY
	PIPE			
1	PIPE Sch 120 ASTM A106-B	4	74.30.03.159.1	16.7m
	FITTINGS			
2	TEE EQUAL BW Sch 120 ASTM A234-WPB	4 x 4	76.30.81.650.1	1
3	TEE REDUCING BW Sch 120 X Sch 160 ASTM A234-WPB	4 x 2	76.30.88.161.1	2
4	BRANCH FITTING PLAIN Sch 120xXXS ASTM A105	4 x 1	76.72.69.361.1	1
5	ELBOW 90 DEG LR BW Sch 120 ASTM A234-WPB	4	76.30.42.650.1	1
	FLANGES			
6	WELDING NECK FLANGE Sch 120 300# ASTM A105	4	76.62.78.634.1	5
7	WELDING NECK FLANGE Sch 160 300# ASTM A105	2	76.62.78.660.1	2
	PIPE ANNOTATIONS			
8	WEAR PLATE TYPE-421 PAD L 550mm	4		1
9	PIPE STOP TYPE-602	4		1

ERECTION MATERIALS

PT NO	COMPONENT DESCRIPTION	SIZE (Inch)	ITEM CODE	QTY
	FITTINGS			
10	Spectacle blind 300# ASTM A516-60/65/70	4	76.89.62.054.1	1
	GASKETS			
11	GASKET SPIRAL WOUND 300# AISI 316, Graphite CS centring/SS inner ring	4	85.41.36.370.1	6
	BOLTS			
12	130 STUDBOLT WITH NUTS ASTM A193-B7M/A194-2HM	3/4	81.38.66.334.1	8
13	120 STUDBOLT WITH NUTS ASTM A193-B7M/A194-2HM	3/4	81.38.66.332.1	32
	VALVES / IN-LINE ITEMS			
14	GATE VALVE FLGD 300# Body: ASTM A105/A216-WCB/WCC Trim: Alloy 825	4	77.XK.BP.B07.9	2
	PIPE ANNOTATIONS			
15	Pipe Rest XRT01	4		7
16	GUIDE PDO-TYPE-604A/B - 2 x L50x50x6x80HIGH	4		3

www.pdo.co.om

HOLDS :

1. NOT ASSIGNEDELEVATION. LOCATION & SUPPORT HOLD AT PIPELINE/PIPING INTERFACE.
2. INSULATION GASKET
3. WEAR PLATE LENGTH & PIPE STOP LENGTH
4. 88-YIQ-10013/15 VENDOR DRAWING
5. STRESS ANALYSIS

NOTES:

1. ALL DIMENSIONS, ELEVATIONS & CO-ORDINATES ARE IN MM

UED
ENGINEERING DIRECTORATE

MATERIAL	Carbon steel sour					PIPING CLASS	31441C4
INSULATION TYPE	PP	STRESS ANALYSIS	Yes	PAINTING SYSTEM	PCS-2		
INSULATION THICKNESS	50	INSPECTION CLASS	Class-1b	COLOUR	SP-1166		
HEAT TRACING	-	FLUID CATEGORY					
STRESS RELIEVE	-	RATING	300#				

LINE CONDITIONS

	DESIGN	TEST
PRESS kPa (g)	4140	7665
TEMP (°C)	260/5	
TEST TYPE	Water	

PEFS	AML-88-PDFEED-PX-2365-00028-0001	02	25.05.22	APPROVED FOR CONSTRUCTION (WITH HOLDS)	RDR	BS	BS		
STRESS CALC NO	-	01	13.03.22	APPROVED FOR CONSTRUCTION (WITH HOLDS)	RRR	VKR	BS		
GA	AML-88-PDFEED-MP-4033-00010-0017/0016	REV	DATE	DESCRIPTION	DRN.	CHKD.	APPD.	STRESS APP.	CLIENT APP.
REFERENCE DRAWINGS & DOCUMENTS		REVISION DETAILS							

شركة تنمية نفط عمان
Petroleum Development Oman

PROJECT TITLE
AMAL WEST DEVELOPMENT OFF-PLOT FACILITIES

AREA	PLANT	WBS No.
AMAL WEST	AMAL WEST PHASE 2A3_88-MS-10001A	-
MODEL AREA	LINE No.	PROJECT CODE
ASIM-1835-CU	4"-P8810203-31441C4-PP	SST000AL0329-AC

BY	DATE	BY	DATE	BY	DATE	BY	DATE	BY	DATE
RRR	13.03.22	VKR	13.03.22	BS	13.03.22	TNJ	13.03.22		

DRAWING NO	SHEET	REV
AML-88-PDFEED-MP-2343-00010-0315	1 OF 1	02